



All top of steel levels and exact steel locations to be reviewed and agreed by the Client & the builder (inc. Architect if required). These drawings provide the steel element sizes with maximum clear spans.

Notes:
Refer to drawing SGN for all general notes

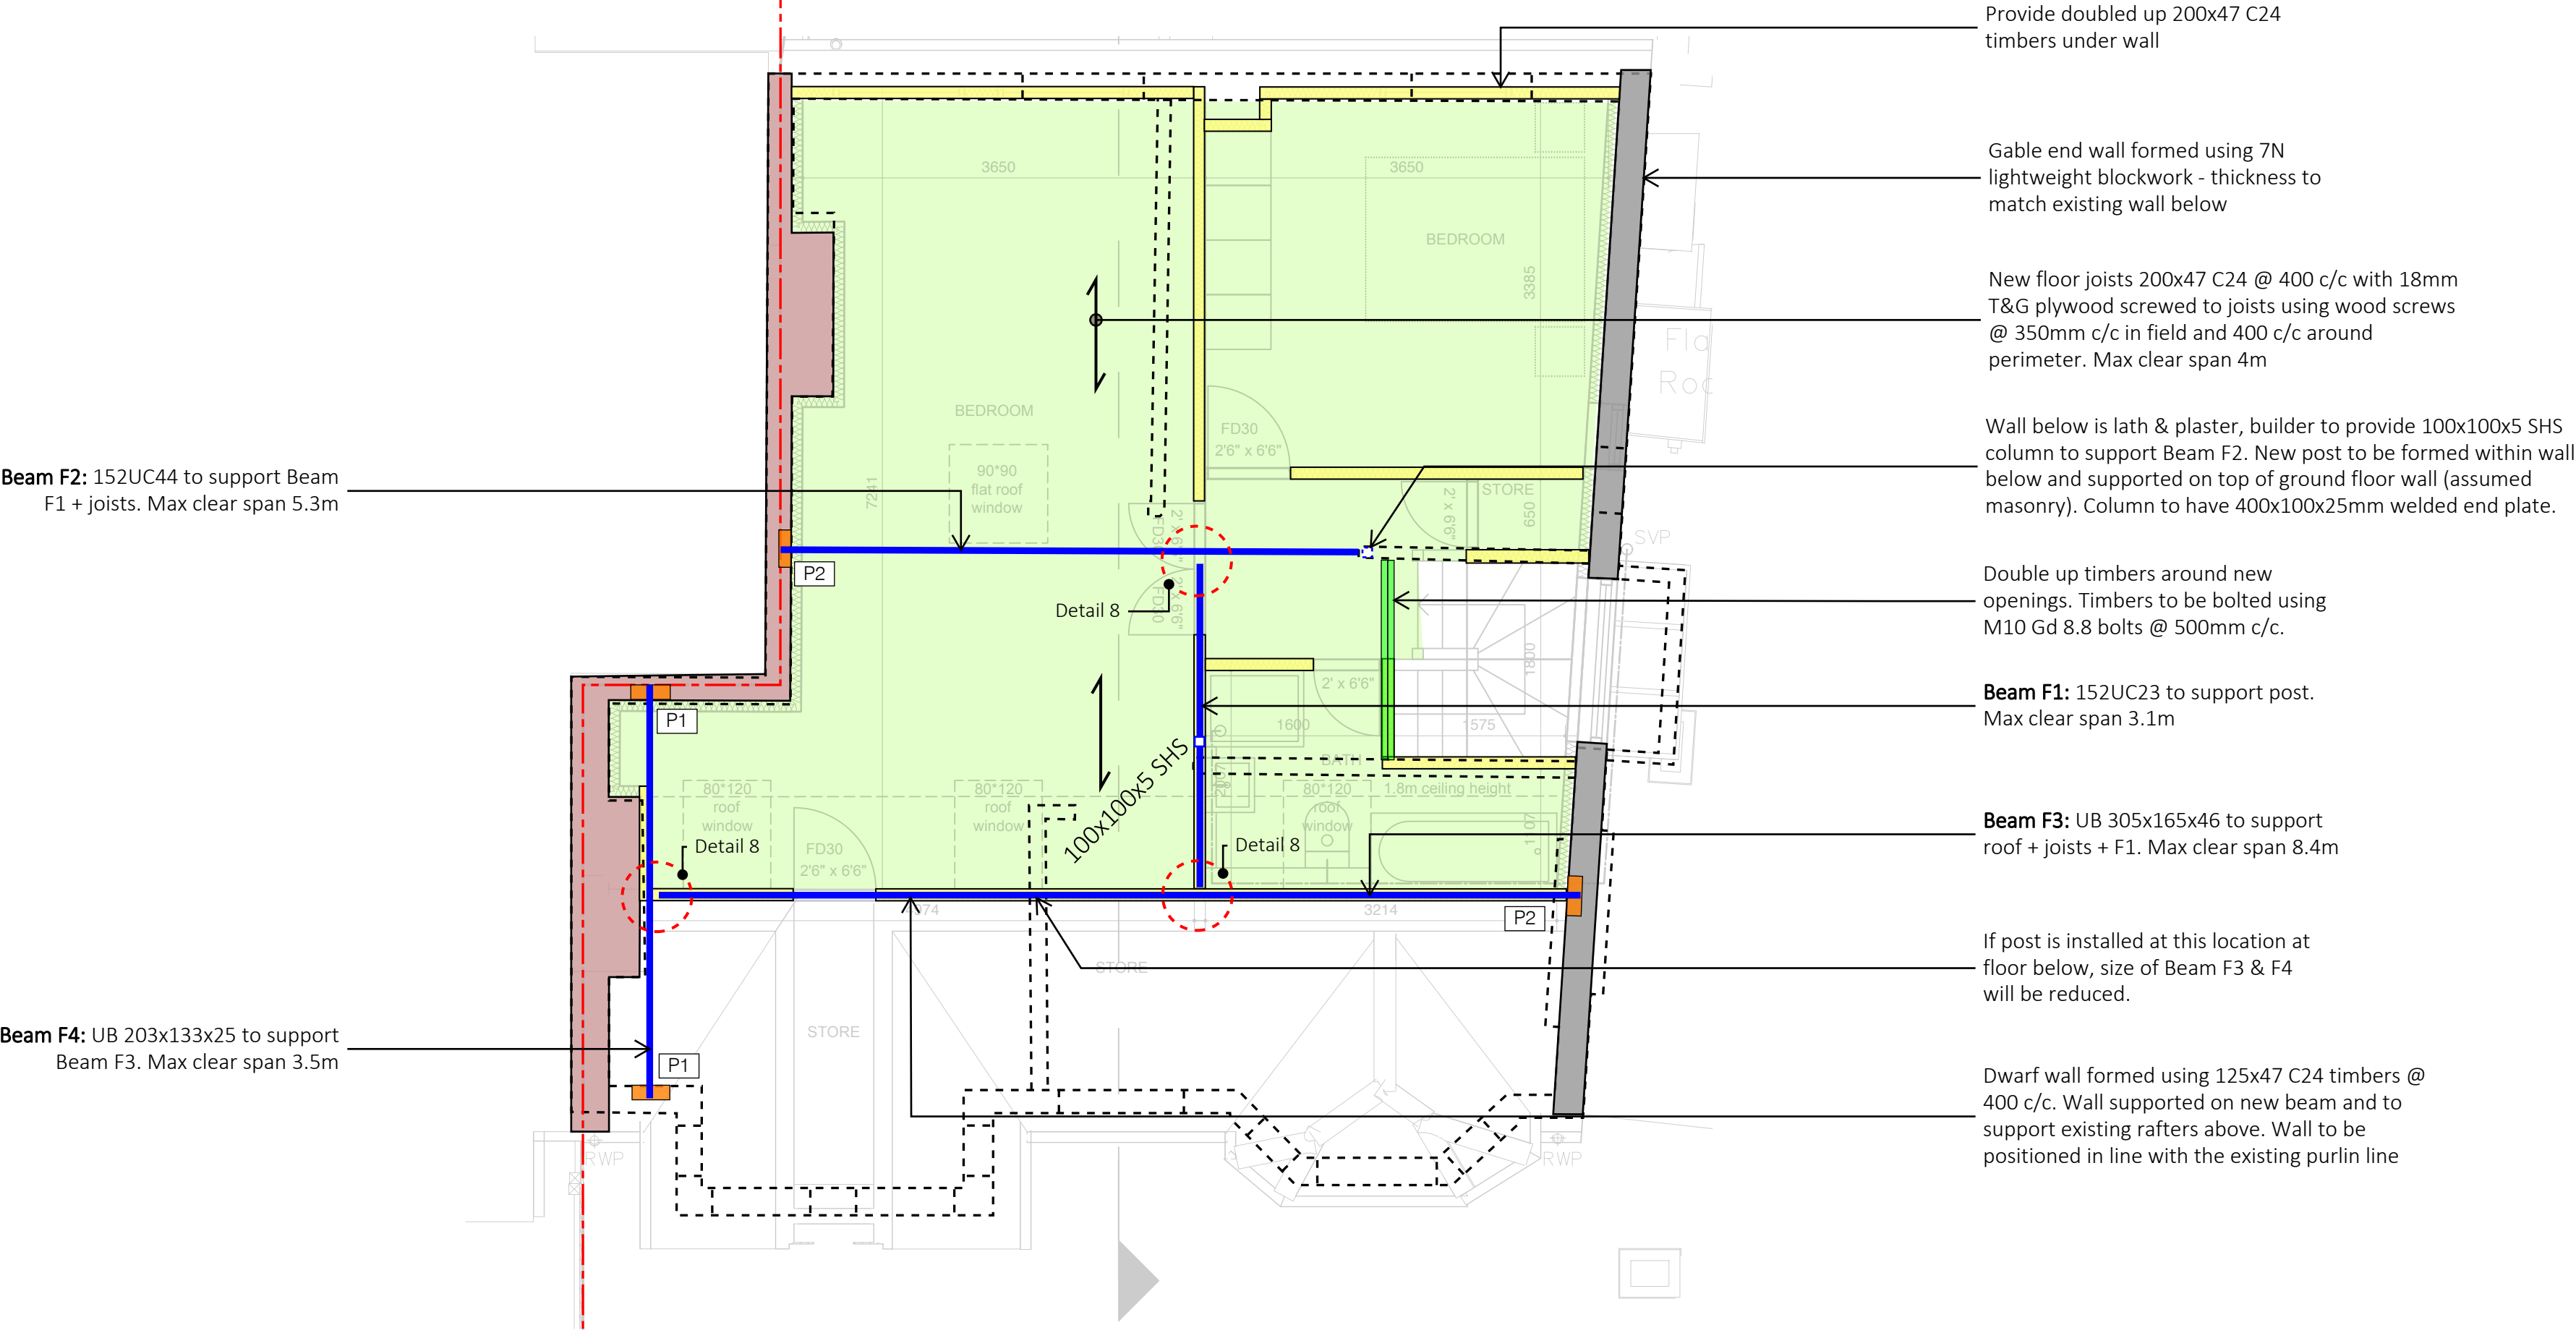

LINTEL SCHEDULE	
Ref	Type
L1	Catnic CH90/100 or similar
L2	R21 - 140x215 Supreme Lintel
Lintel to be based on Architects cavity width	

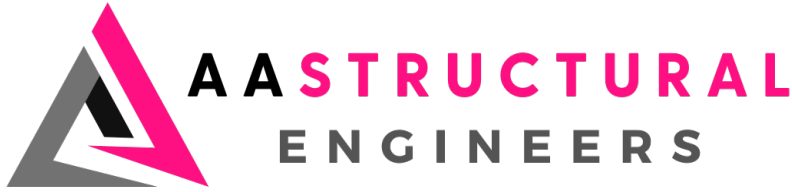

Website: www.aastructuralengineers.com
Phone: 07501460681
Company registration No: 13400301

STRUCTURAL DRAWINGS

Job Title: 217 Boston Rd London W7 2AA

Drawings No:

Drawing Title: Proposed Loft Floor Plan

S01

Scale: 1:50@A2

Date: Feb 26


Status: PRELIMINARY

Job No: 2025-335

Drawn By: AA

Revision: P1

Notes:
Refer to drawing SGN for all general notes

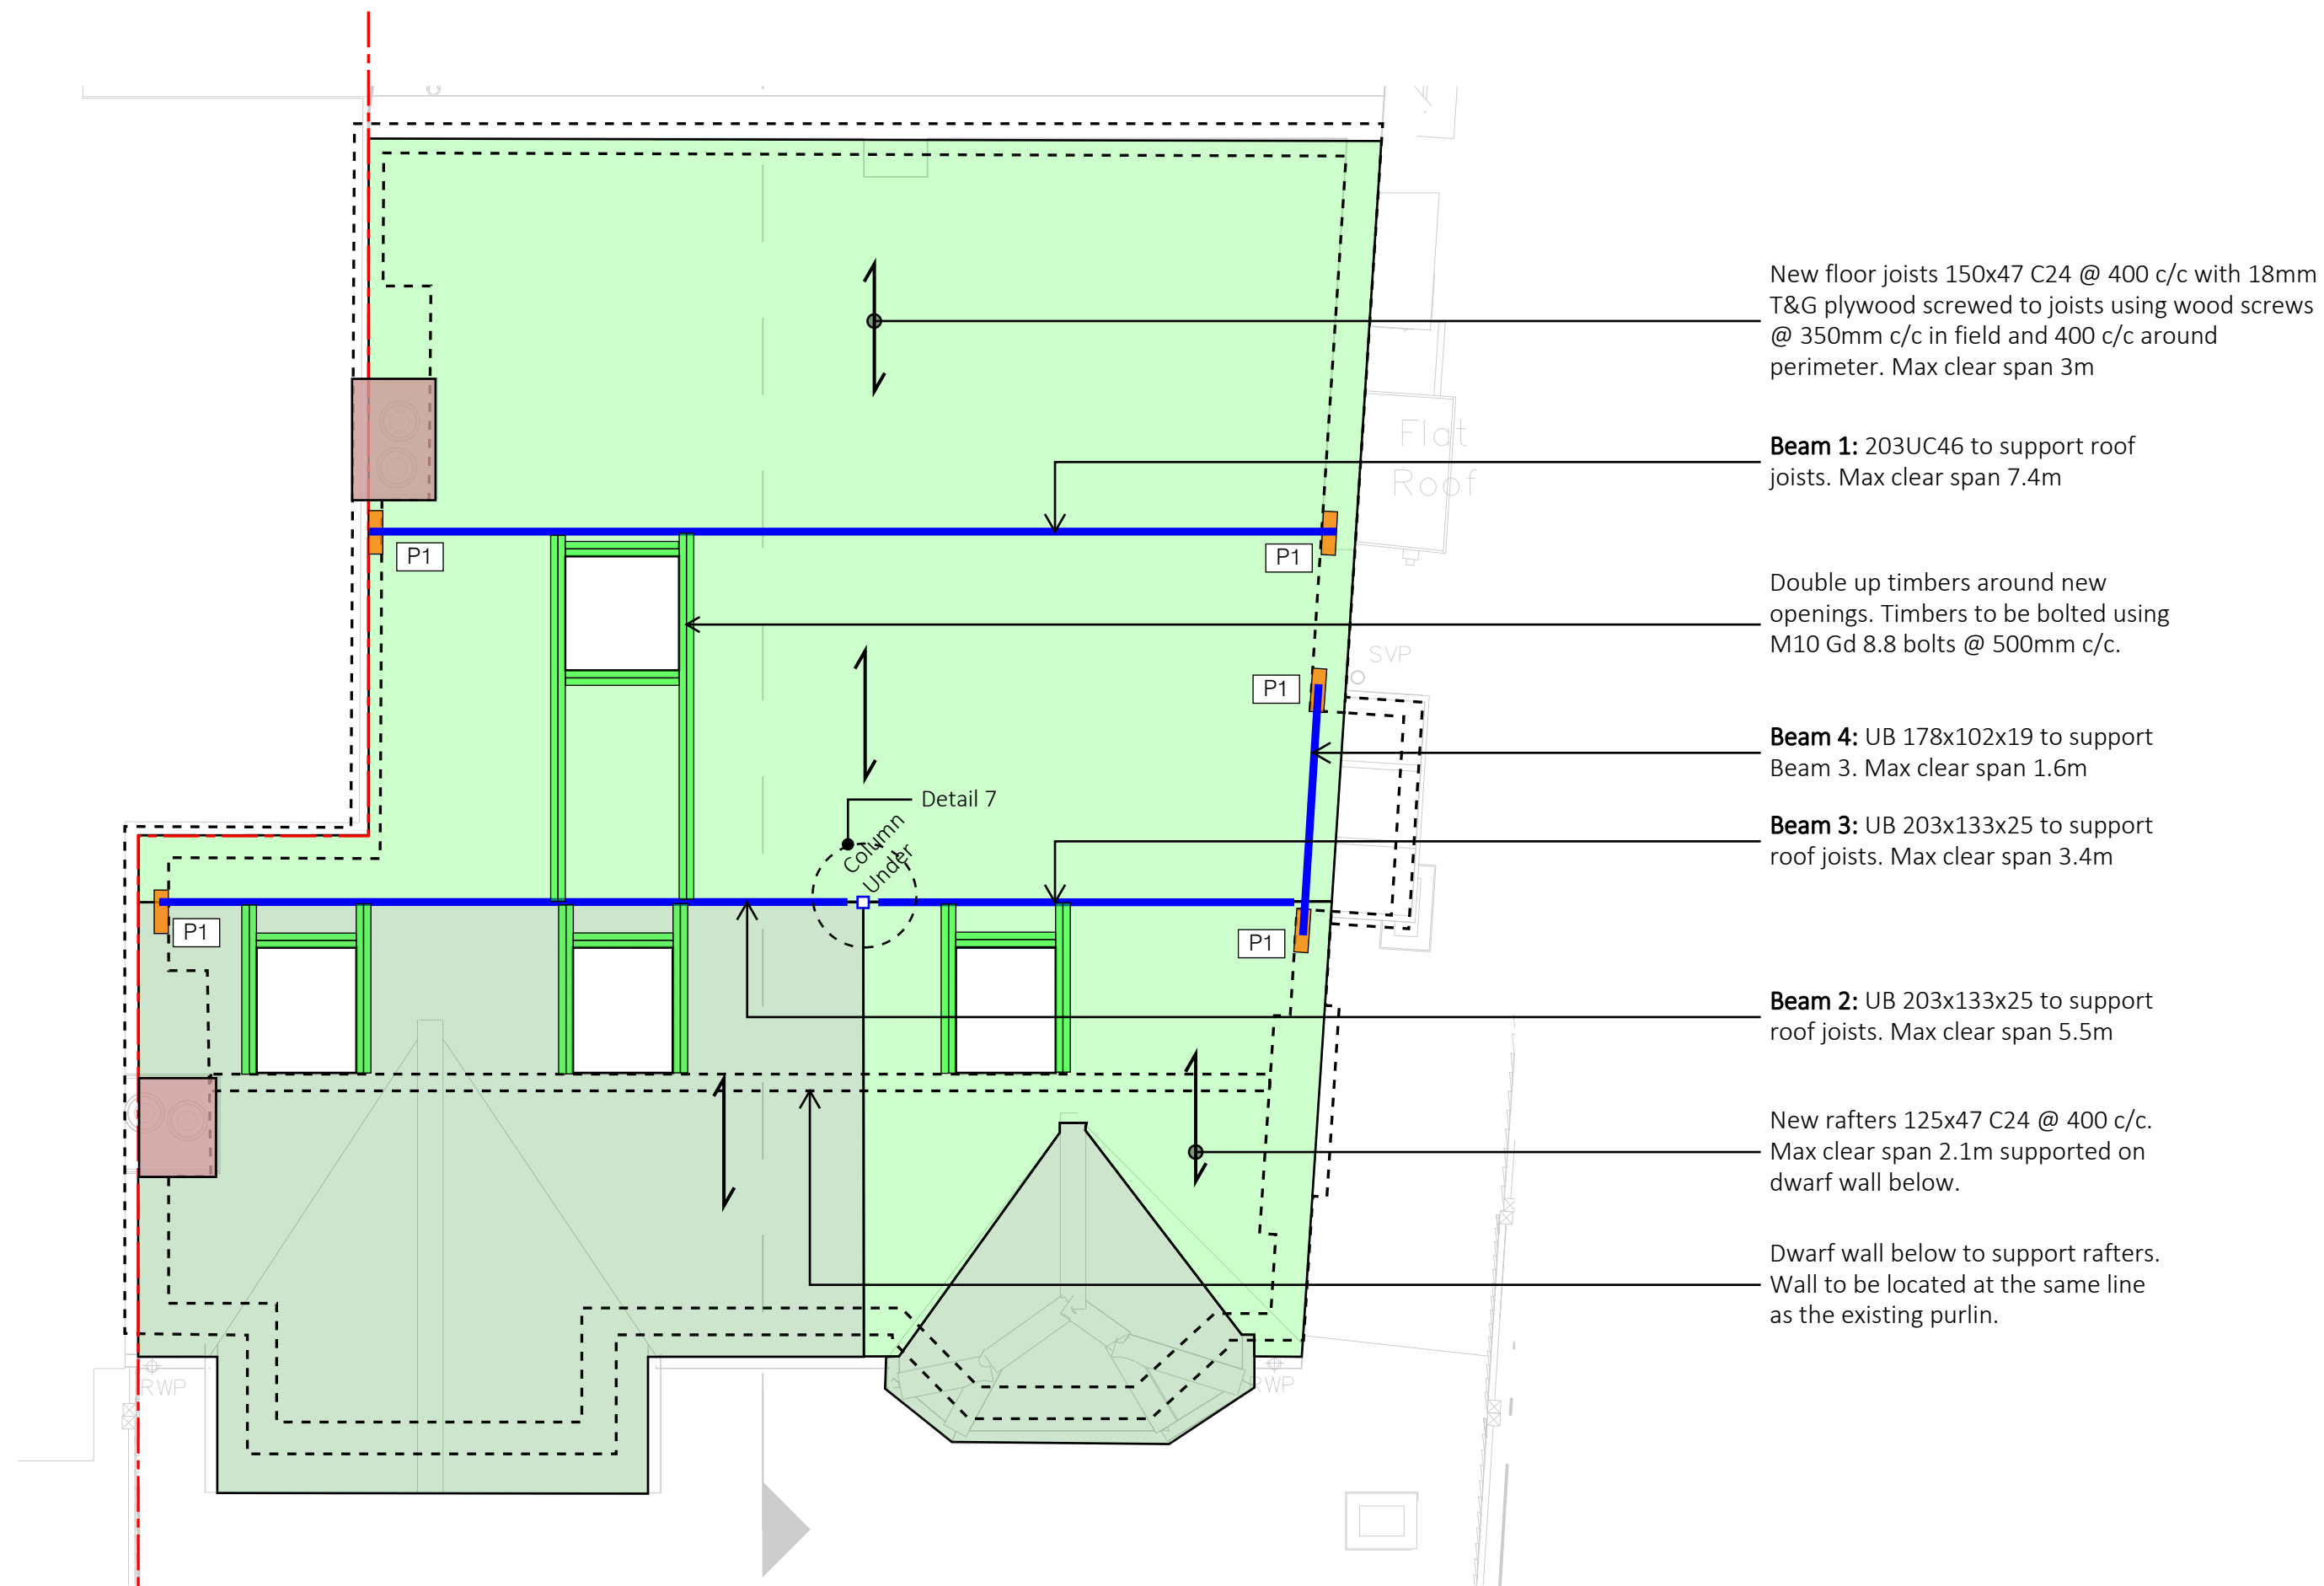

LINTEL SCHEDULE	
Ref	Type
L1	Catnic CH90/100 or similar
L2	R21 - 140x215 Supreme Lintel
Lintel to be based on Architects cavity width	



AA

STRUCTURAL

ENGINEERS


Website: www.aastructuralengineers.com

Phone: 07501460681


Company registration No: 13400301

STRUCTURAL DRAWINGS			
Job Title: 217 Boston Rd London W7 2AA			Drawings No: S02
Drawing Title: Proposed Roof Plan			
Scale: 1:50@A2	Date: Feb 26	Status: PRELIMINARY	
Job No: 2025-335		Drawn By: AA	Revision: P1

Notes:
Refer to drawing SGN for all general notes

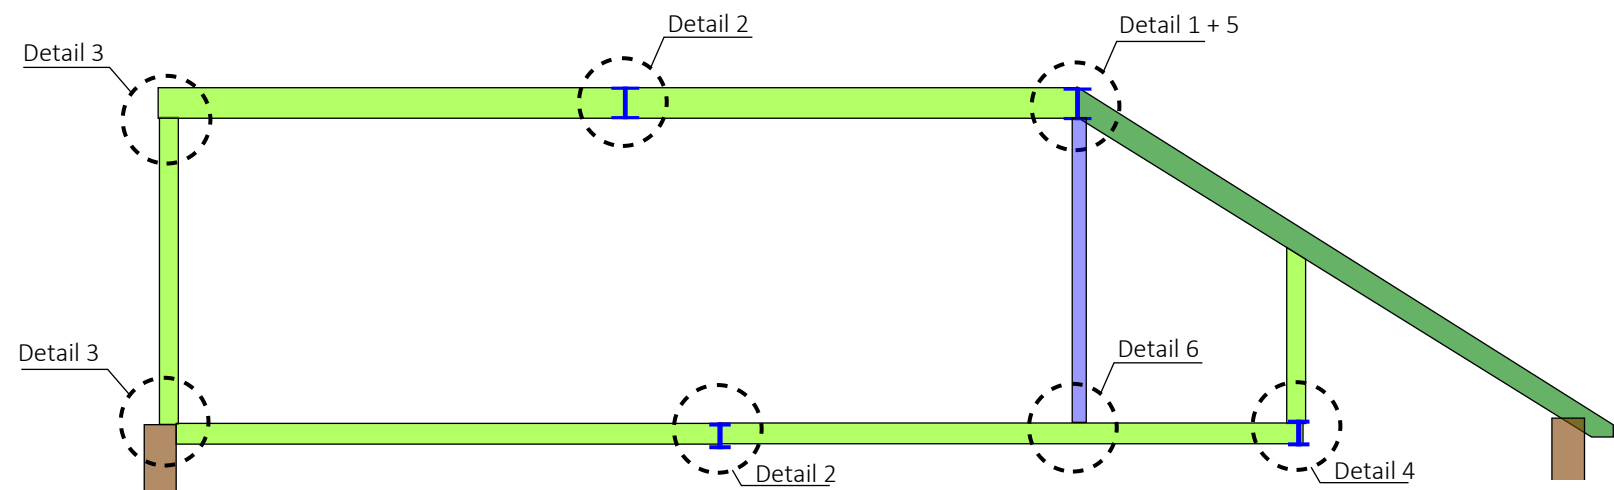


KEY SECTION

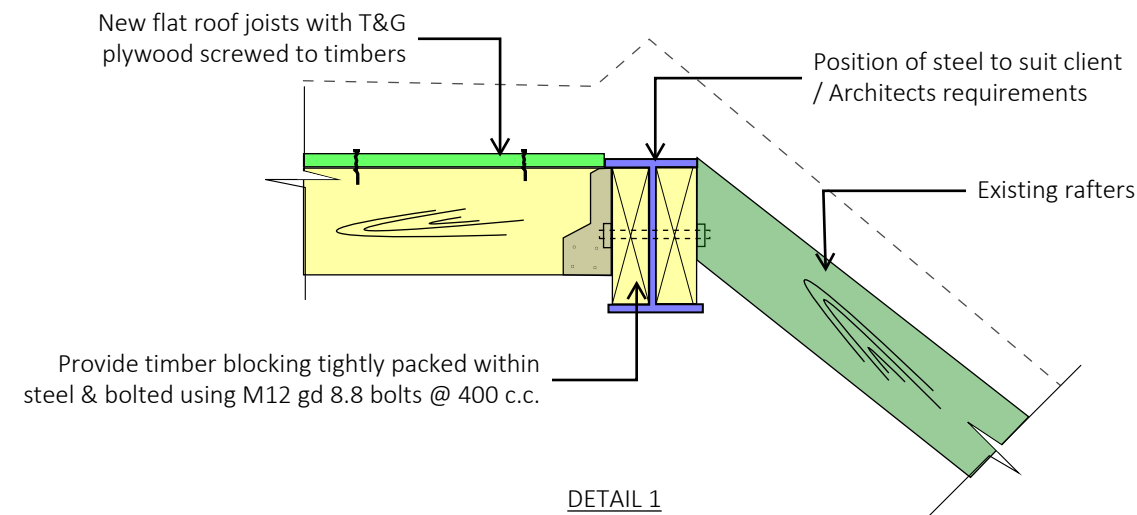


DETAIL 1
UB RIDGE SUPPORT SECTION


Provide timber blocking tightly packed within steel & bolted using M12 gd 8.8 bolts @ 400 c.c.

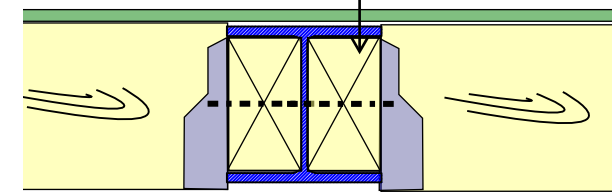

DETAIL 2
BEAM SUPPORT SECTION

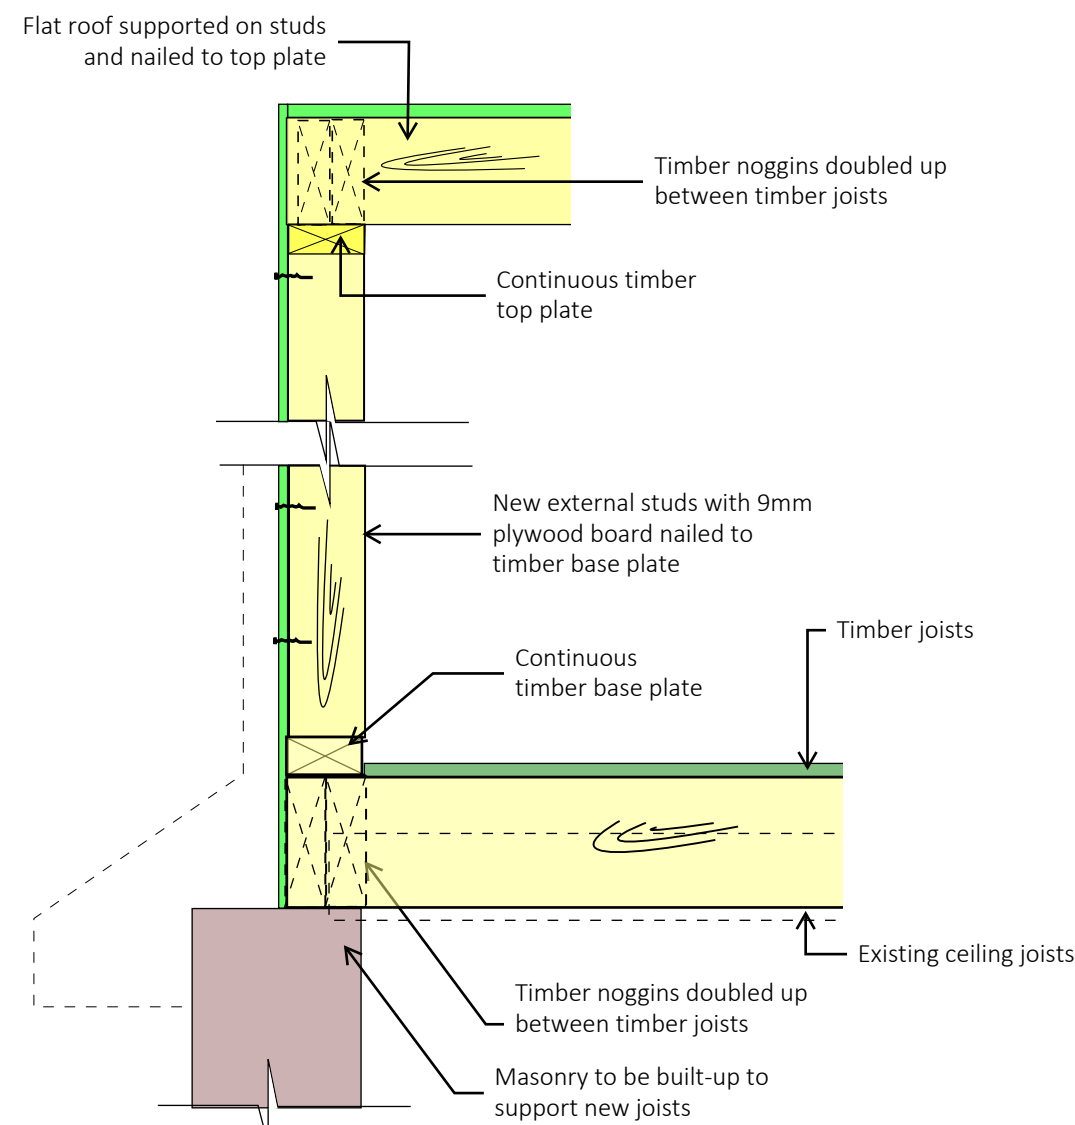


DETAIL 3
REAR STUD WALL TO EXISTING
WALL SECTION

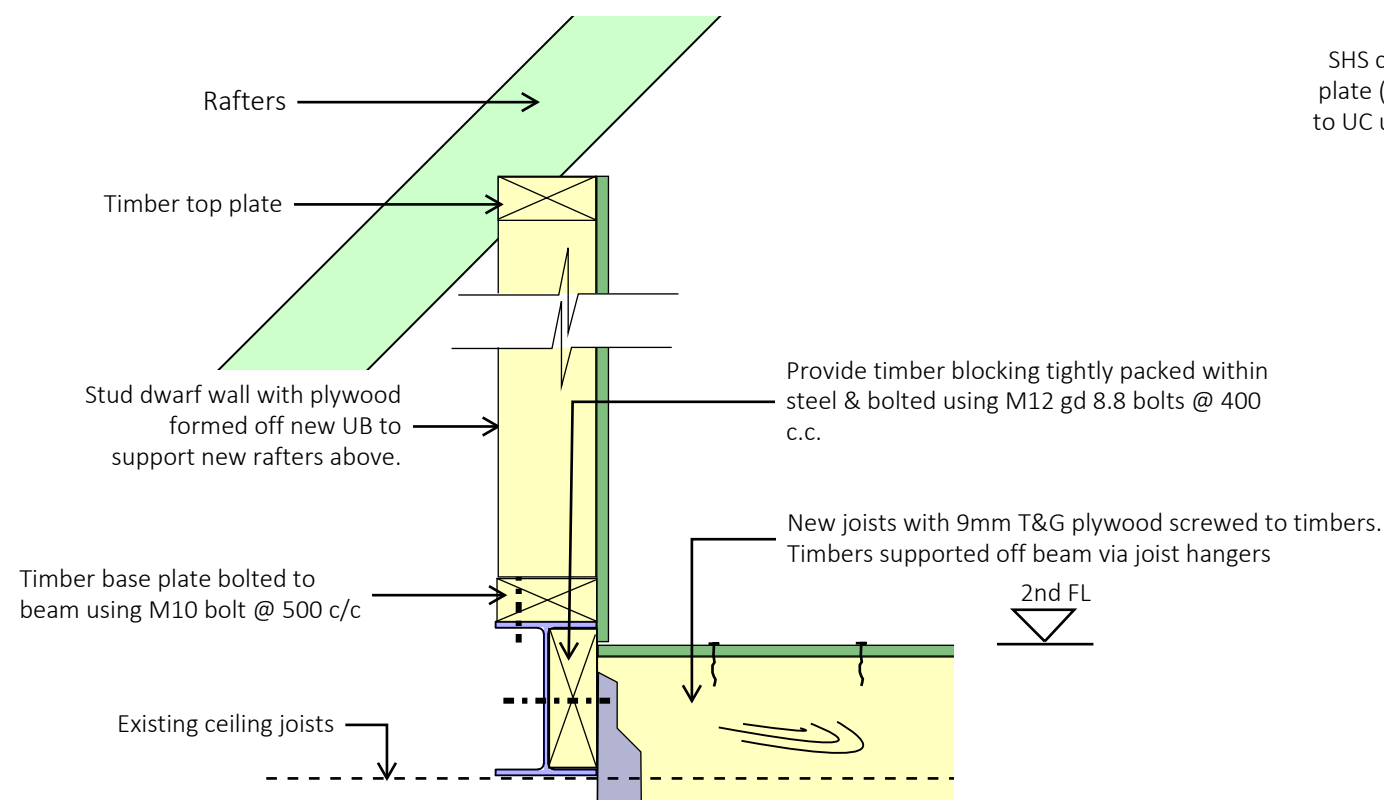


DETAIL 4
FLOOR BEAM SUPPORTING
DRAWF WALL & NEW FLOOR

SHS column with welded capping plate (140x250x15mm thk) bolted to UC using 4No. M12 Gd 8.8 bolts

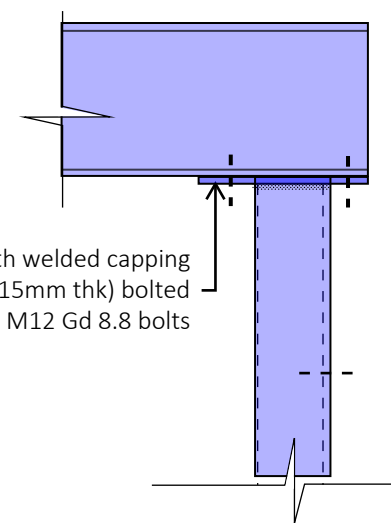


DETAIL 6:
SHS / BEAM CONNECTION
SECTION

UC to UC bolted using 4No. M12 Gd 8.8 bolts. Provide 15mm thk welded end plates. All welds to be 6mm thk CFW

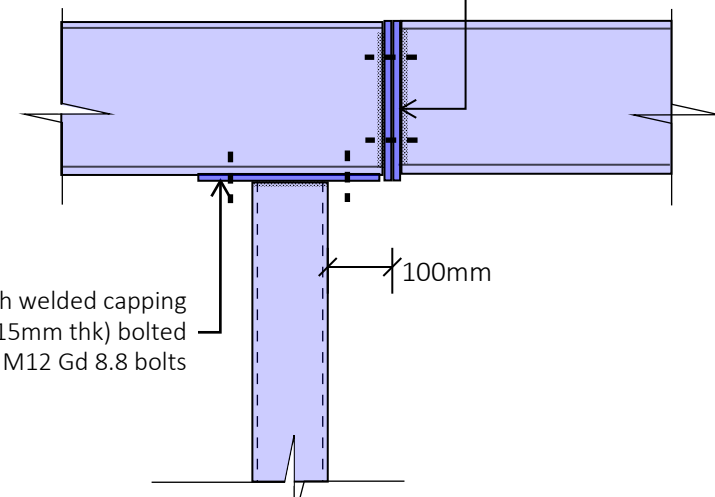

DETAIL 7:
BEAM TO COLUMN
CONNECTION SECTION

Steel column with 15mm welded end plate bolted to beam using 4No. M12 Gd 8.8 bolts

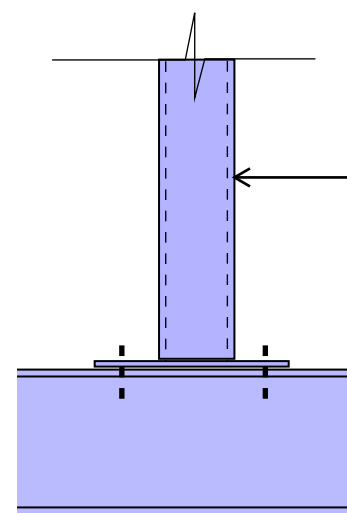


DETAIL 6
COLUMN ON BEAM CONNECTION
ELEVATION



DETAIL 8: BEAM
CONNECTION SECTION

Beam with welded 12mm steel plate and bolted to adjoining Beam using 4No. M12 Gd 8.8 bolts.

All welds to be 6mm continuous fillet welds

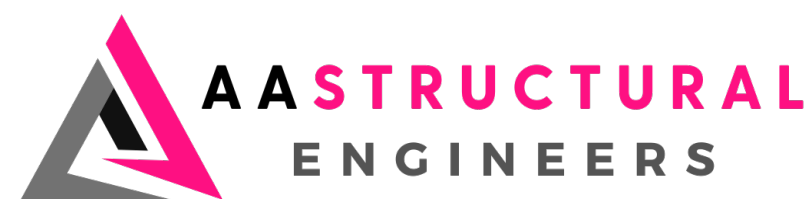

Website: www.aastructuralengineers.com
Phone: 07501460681
Company registration No: 13400301

STRUCTURAL DRAWINGS

Job Title: 217 Boston Rd London W7 2AA

Drawings No:

Drawing Title: Proposed Detail Sheet 1

SK1

Scale: 1:10@A2

Date: Feb 26

Status: PRELIMINARY

Job No: 2025-335

Drawn By: AA

Revision: P1