

GENERAL NOTES

1. THE CONTRACTOR MUST CHECK ALL DIMENSIONS ON SITE BEFORE COMMENCING WORK
2. ANY DISCREPANCIES MUST BE IMMEDIATELY BROUGHT TO THE ATTENTION OF THE DESIGNER
3. ALL WORK MUST CONFORM TO CURRENT BUILDING REGULATIONS, BRITISH STANDARDS & CODES OF PRACTICE AND NHBC STANDARDS
4. THESE DRAWINGS ARE TO BE READ IN CONJUNCTION WITH ALL RELEVANT DESIGNER, ENGINEER OR SPECIALIST DRAWINGS AND SPECIFICATIONS
5. ALL DIMENSIONS ARE IN MILLIMETERS UNLESS STATED OTHERWISE
6. ALL MATERIALS ARE TO BE USED AND INSTALLED IN STRICT COMPLIANCE WITH THE RELEVANT MANUFACTURER'S RECOMMENDATIONS
7. THE CONTRACTOR IS RESPONSIBLE FOR PROVIDING ALL NECESSARY TEMPORARY SUPPORT TO THE BUILDING AND ANY ADJACENT STRUCTURES
8. ALL CONSTRUCTION MUST BE BUILT WITHIN THE ACTUAL PROPERTY BOUNDARIES UNLESS PARTY WALL AGREEMENT ALLOWS OTHERWISE

HATCH/LINE LEGEND (plans and sections)		DRAINAGE ABBREVIATIONS
 concrete	 demolish	mh = manhole
 brickwork	 above/beyond	ic = inspection chamber
 blockwork	 boundary	re = rodding eye
 insulation/ stud partition	 drain	g = gully
		svp = soil vent pipe
		rwp = rain water pipe
		ss = stub stack
		rainwater drainage to contractor design
		electrical layout to client design

REVISION	DESCRIPTION	DATE
----------	-------------	------



DRAW AND PLAN

T: 020 8243 8779

E: info@drawandplan.com

W: www.drawandplan.com

Location

**217 BOSTON ROAD
LONDON
W7 2AA**

Drawing title

GENERAL ARRANGEMENT

Date

22/12/2025

Scale

1:50@A1

Job no.



25100

Dwg no.


EGA002

Revision

-

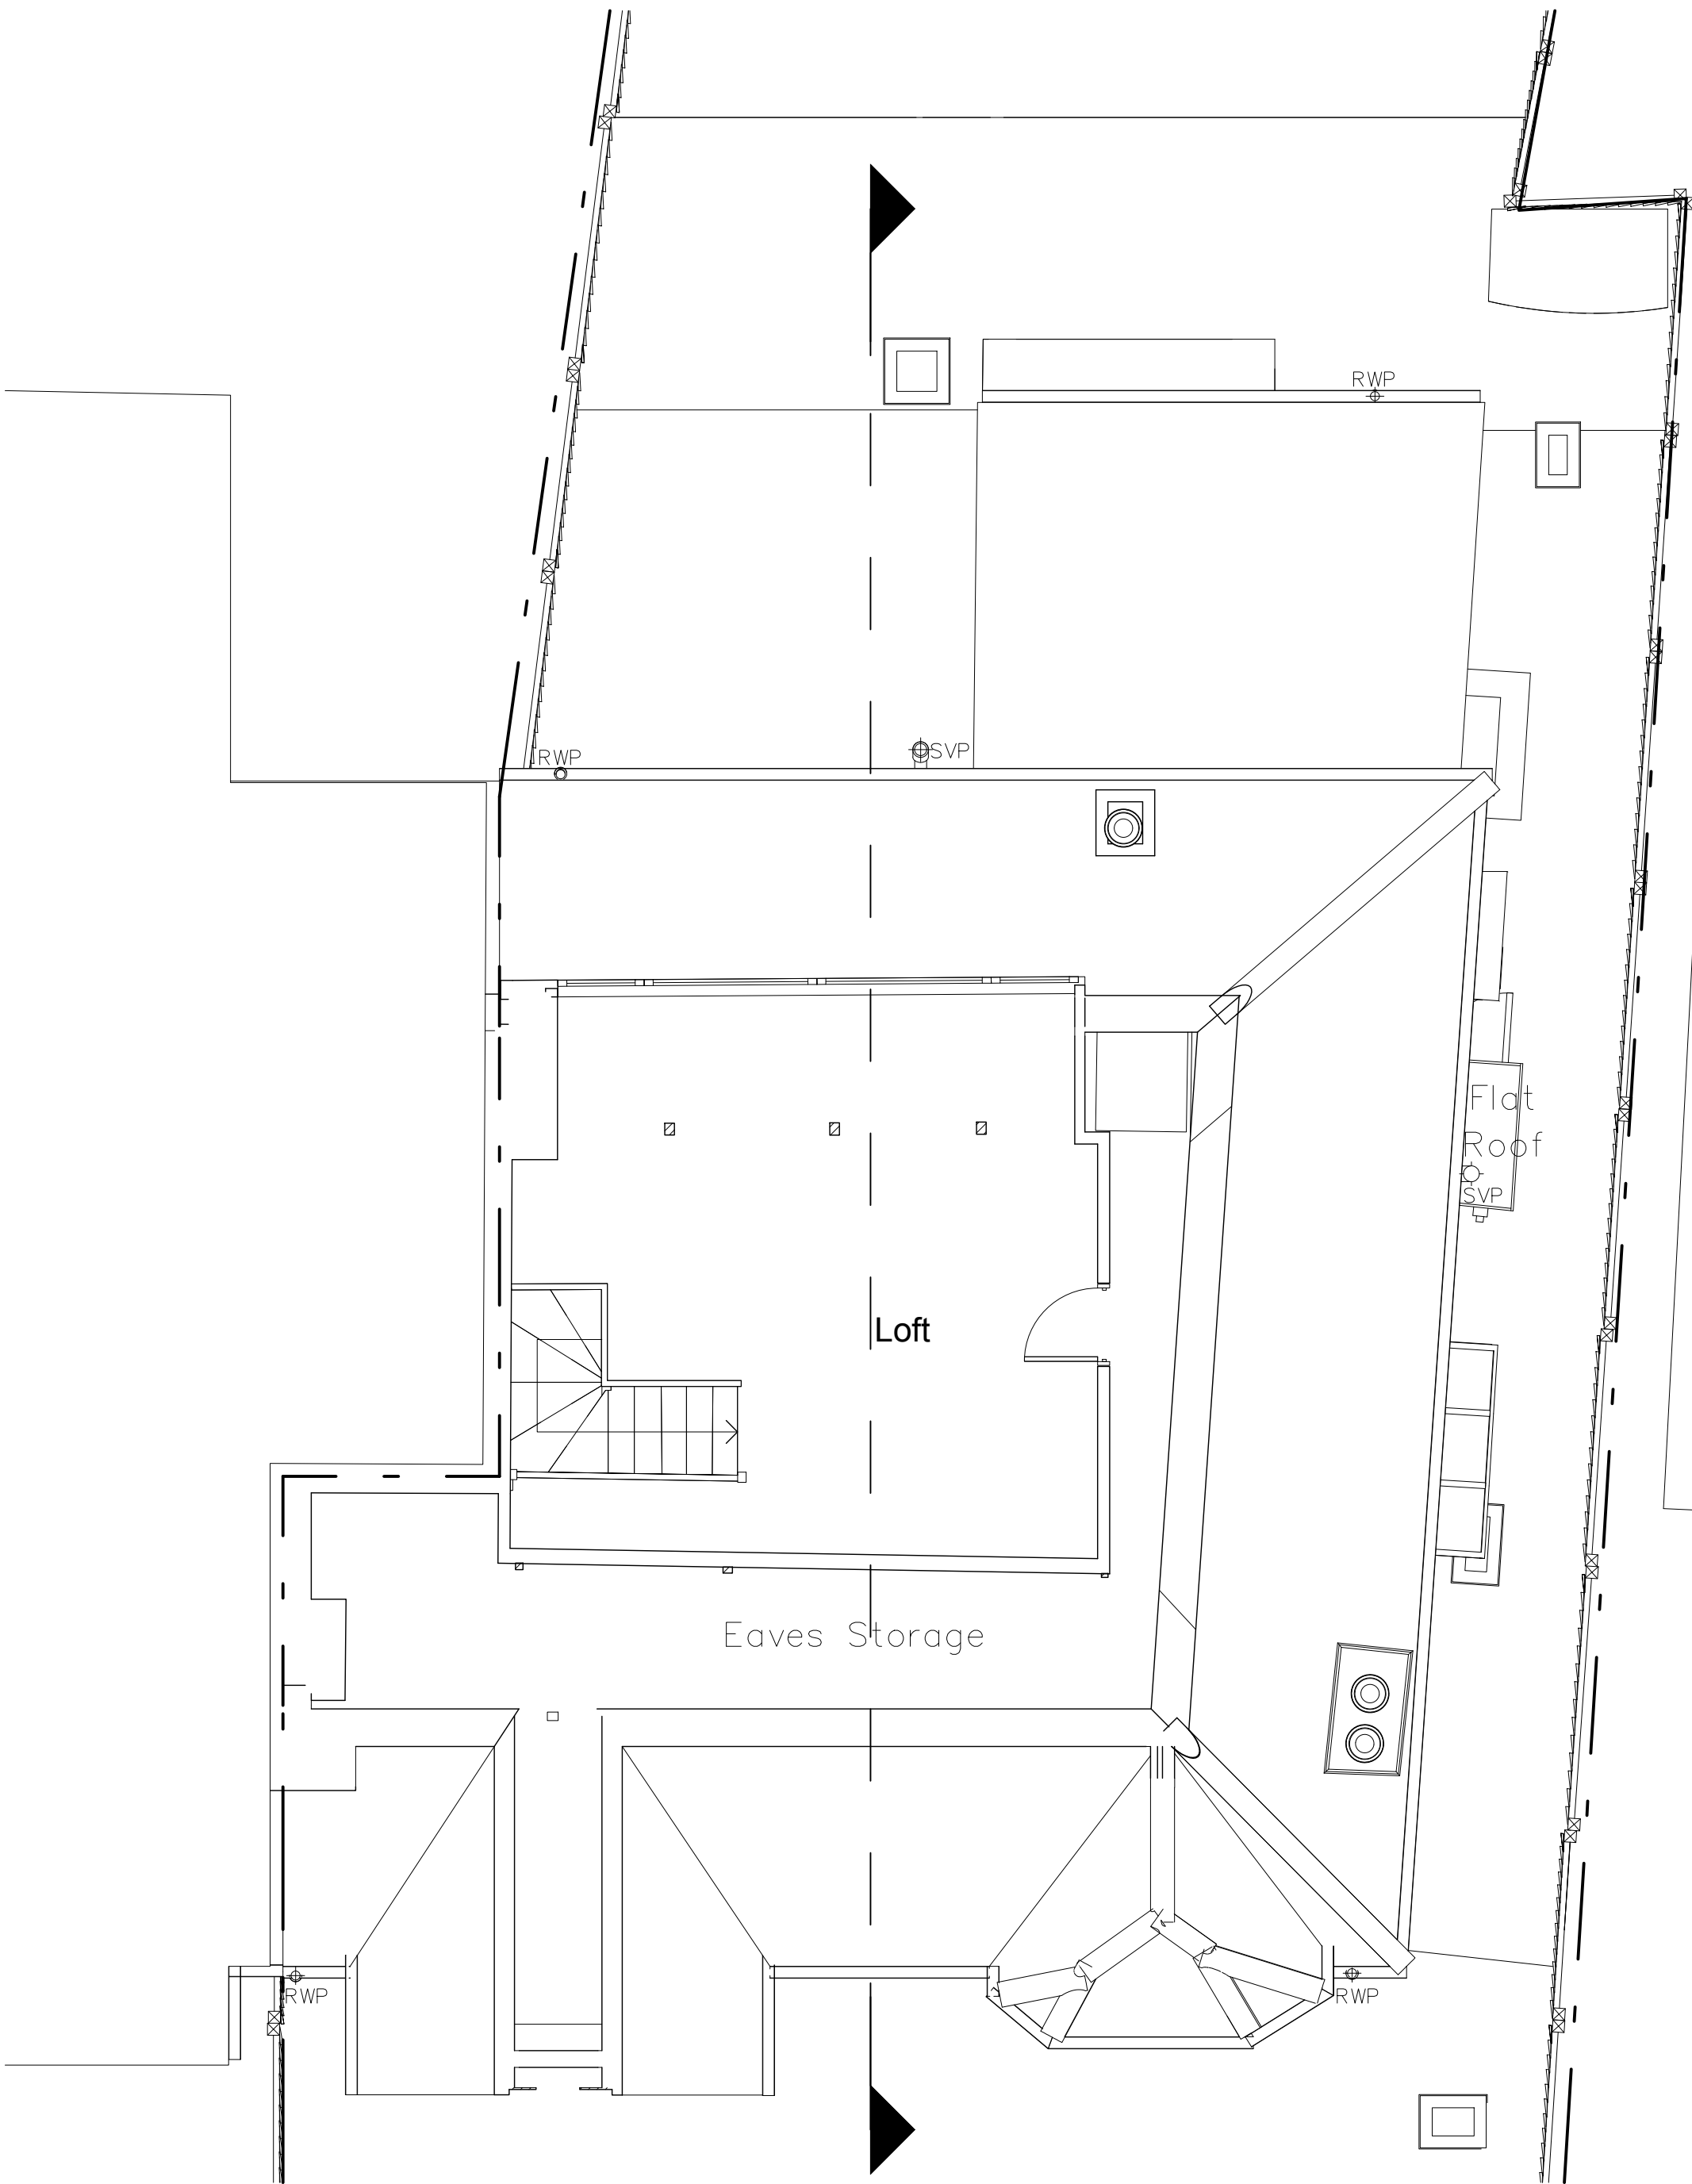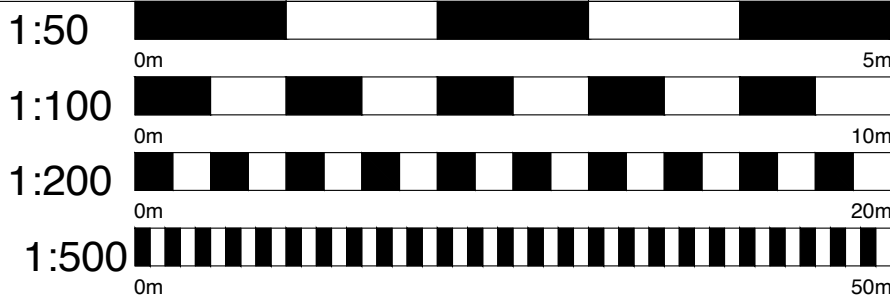

EXISTING LOFT PLAN

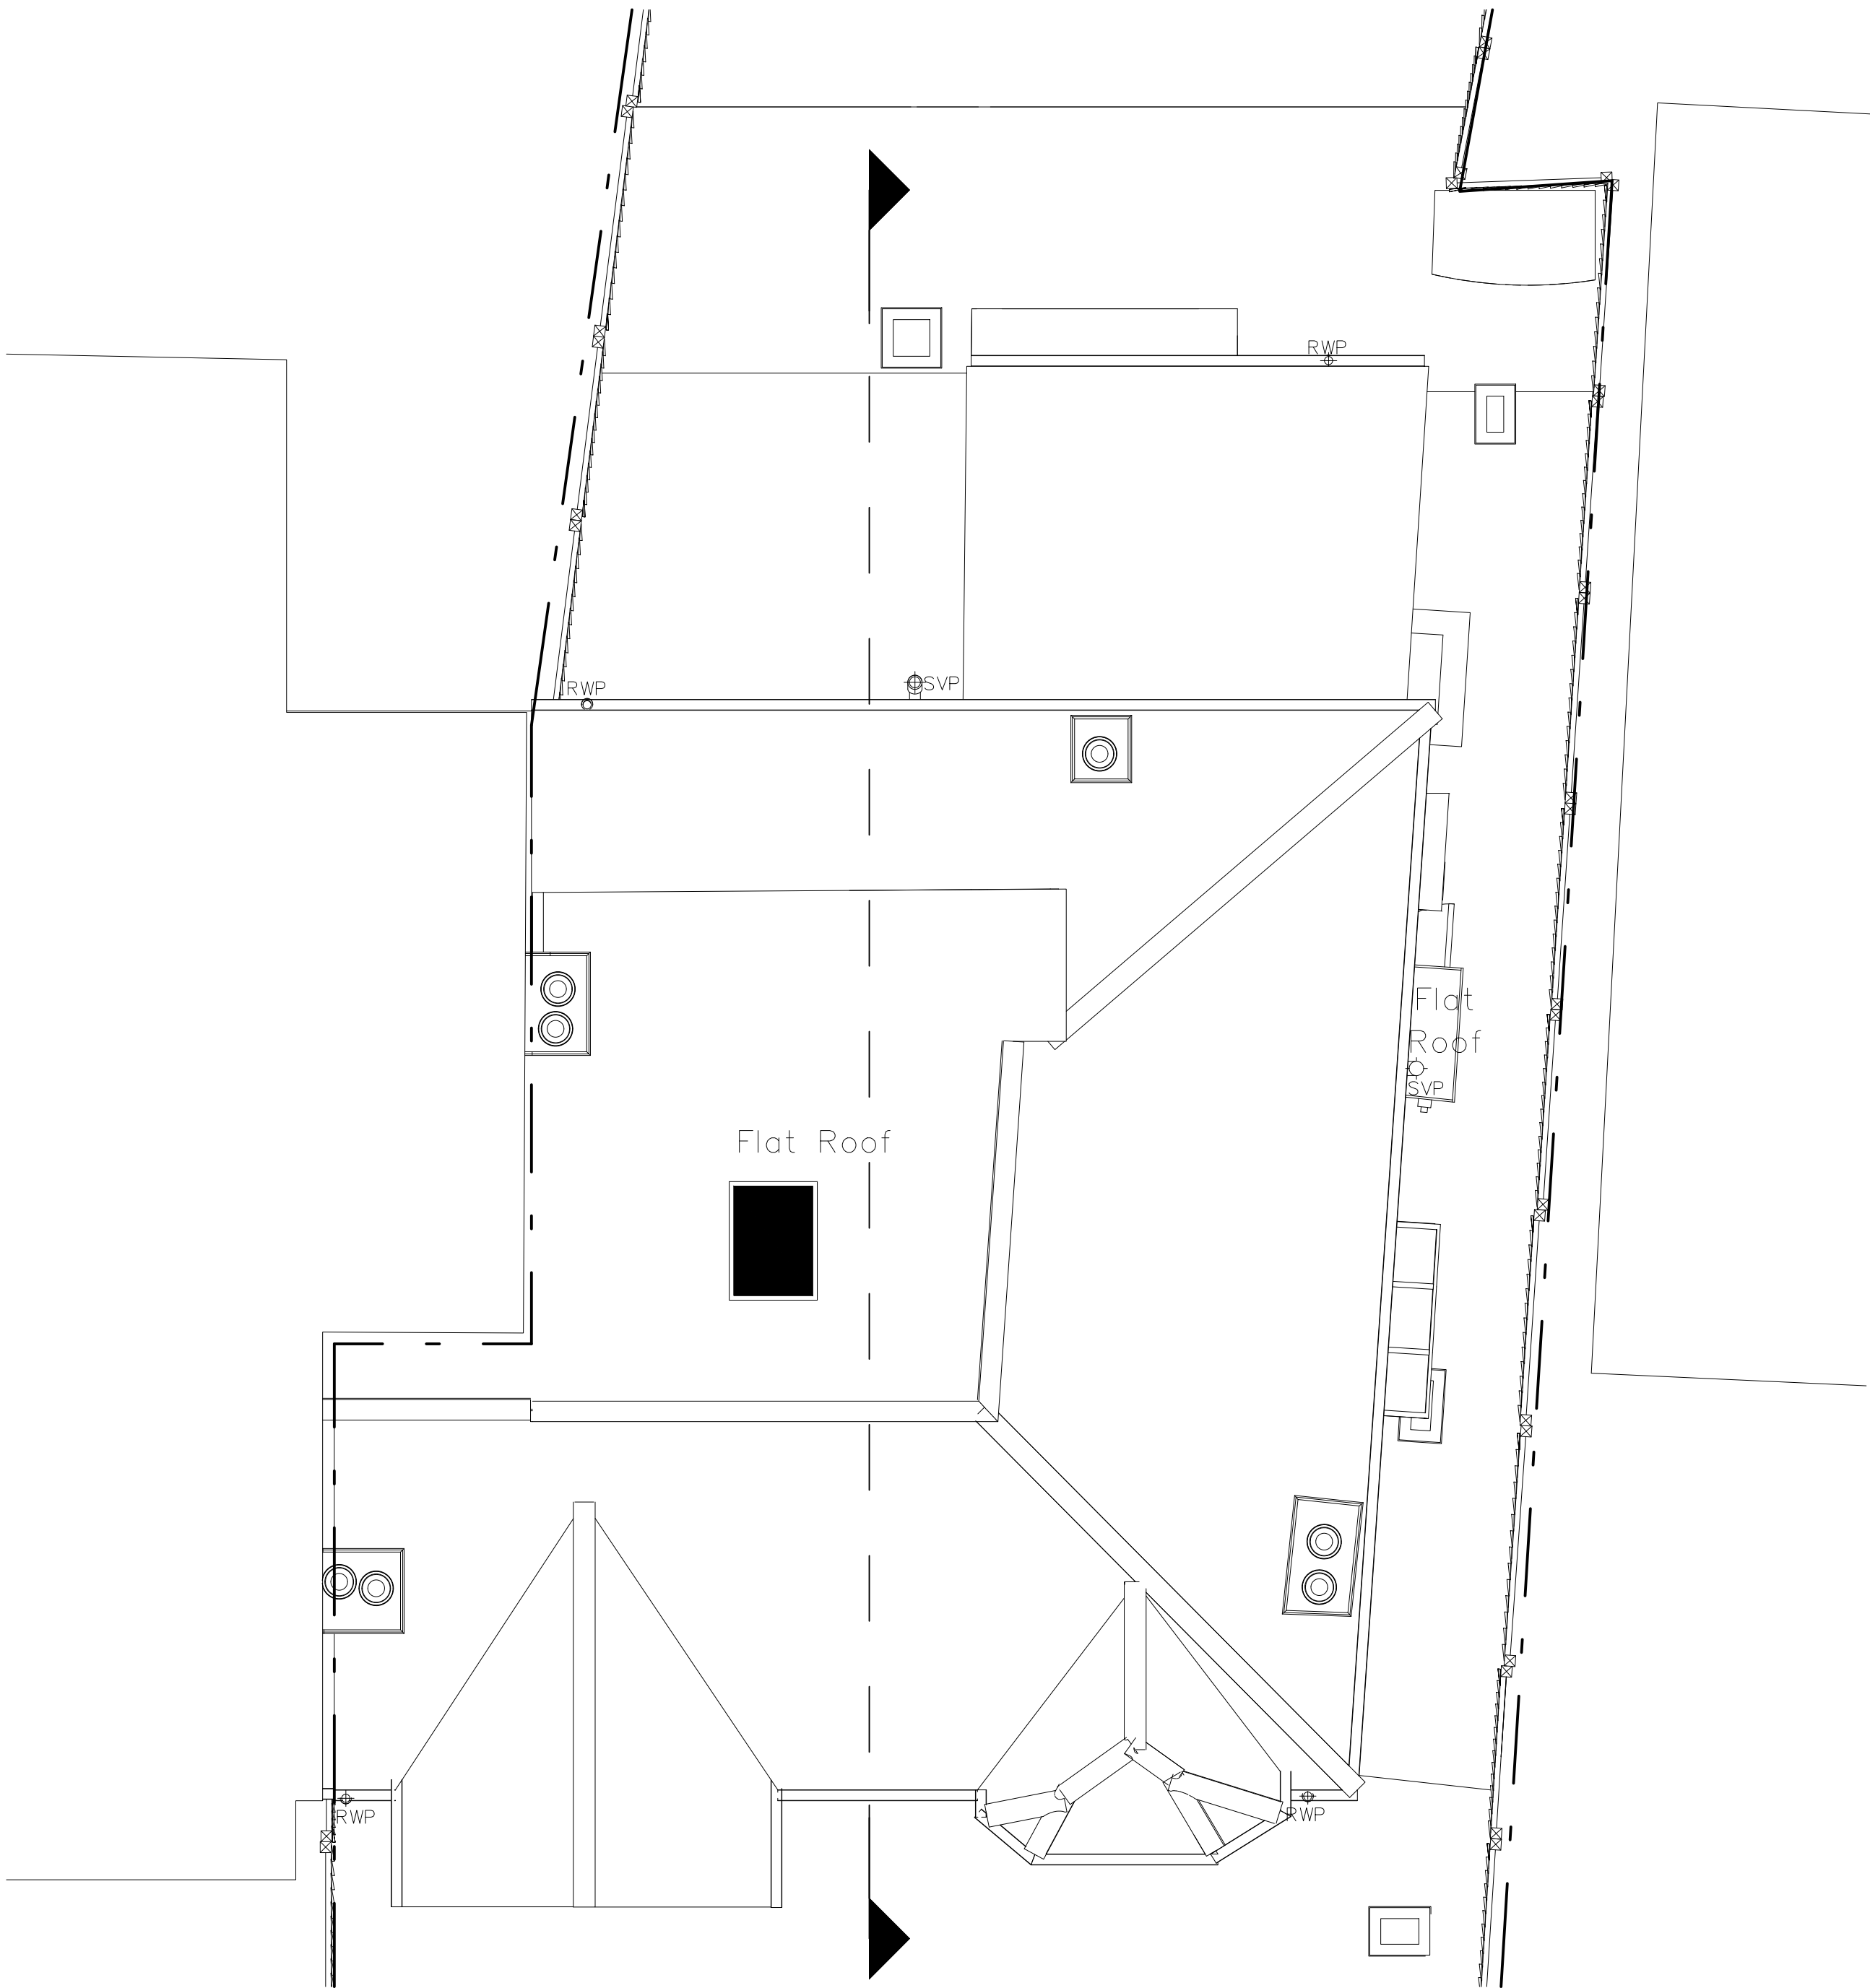

EXISTING ROOF PLAN