




PROPOSED FRONT ELEVATION

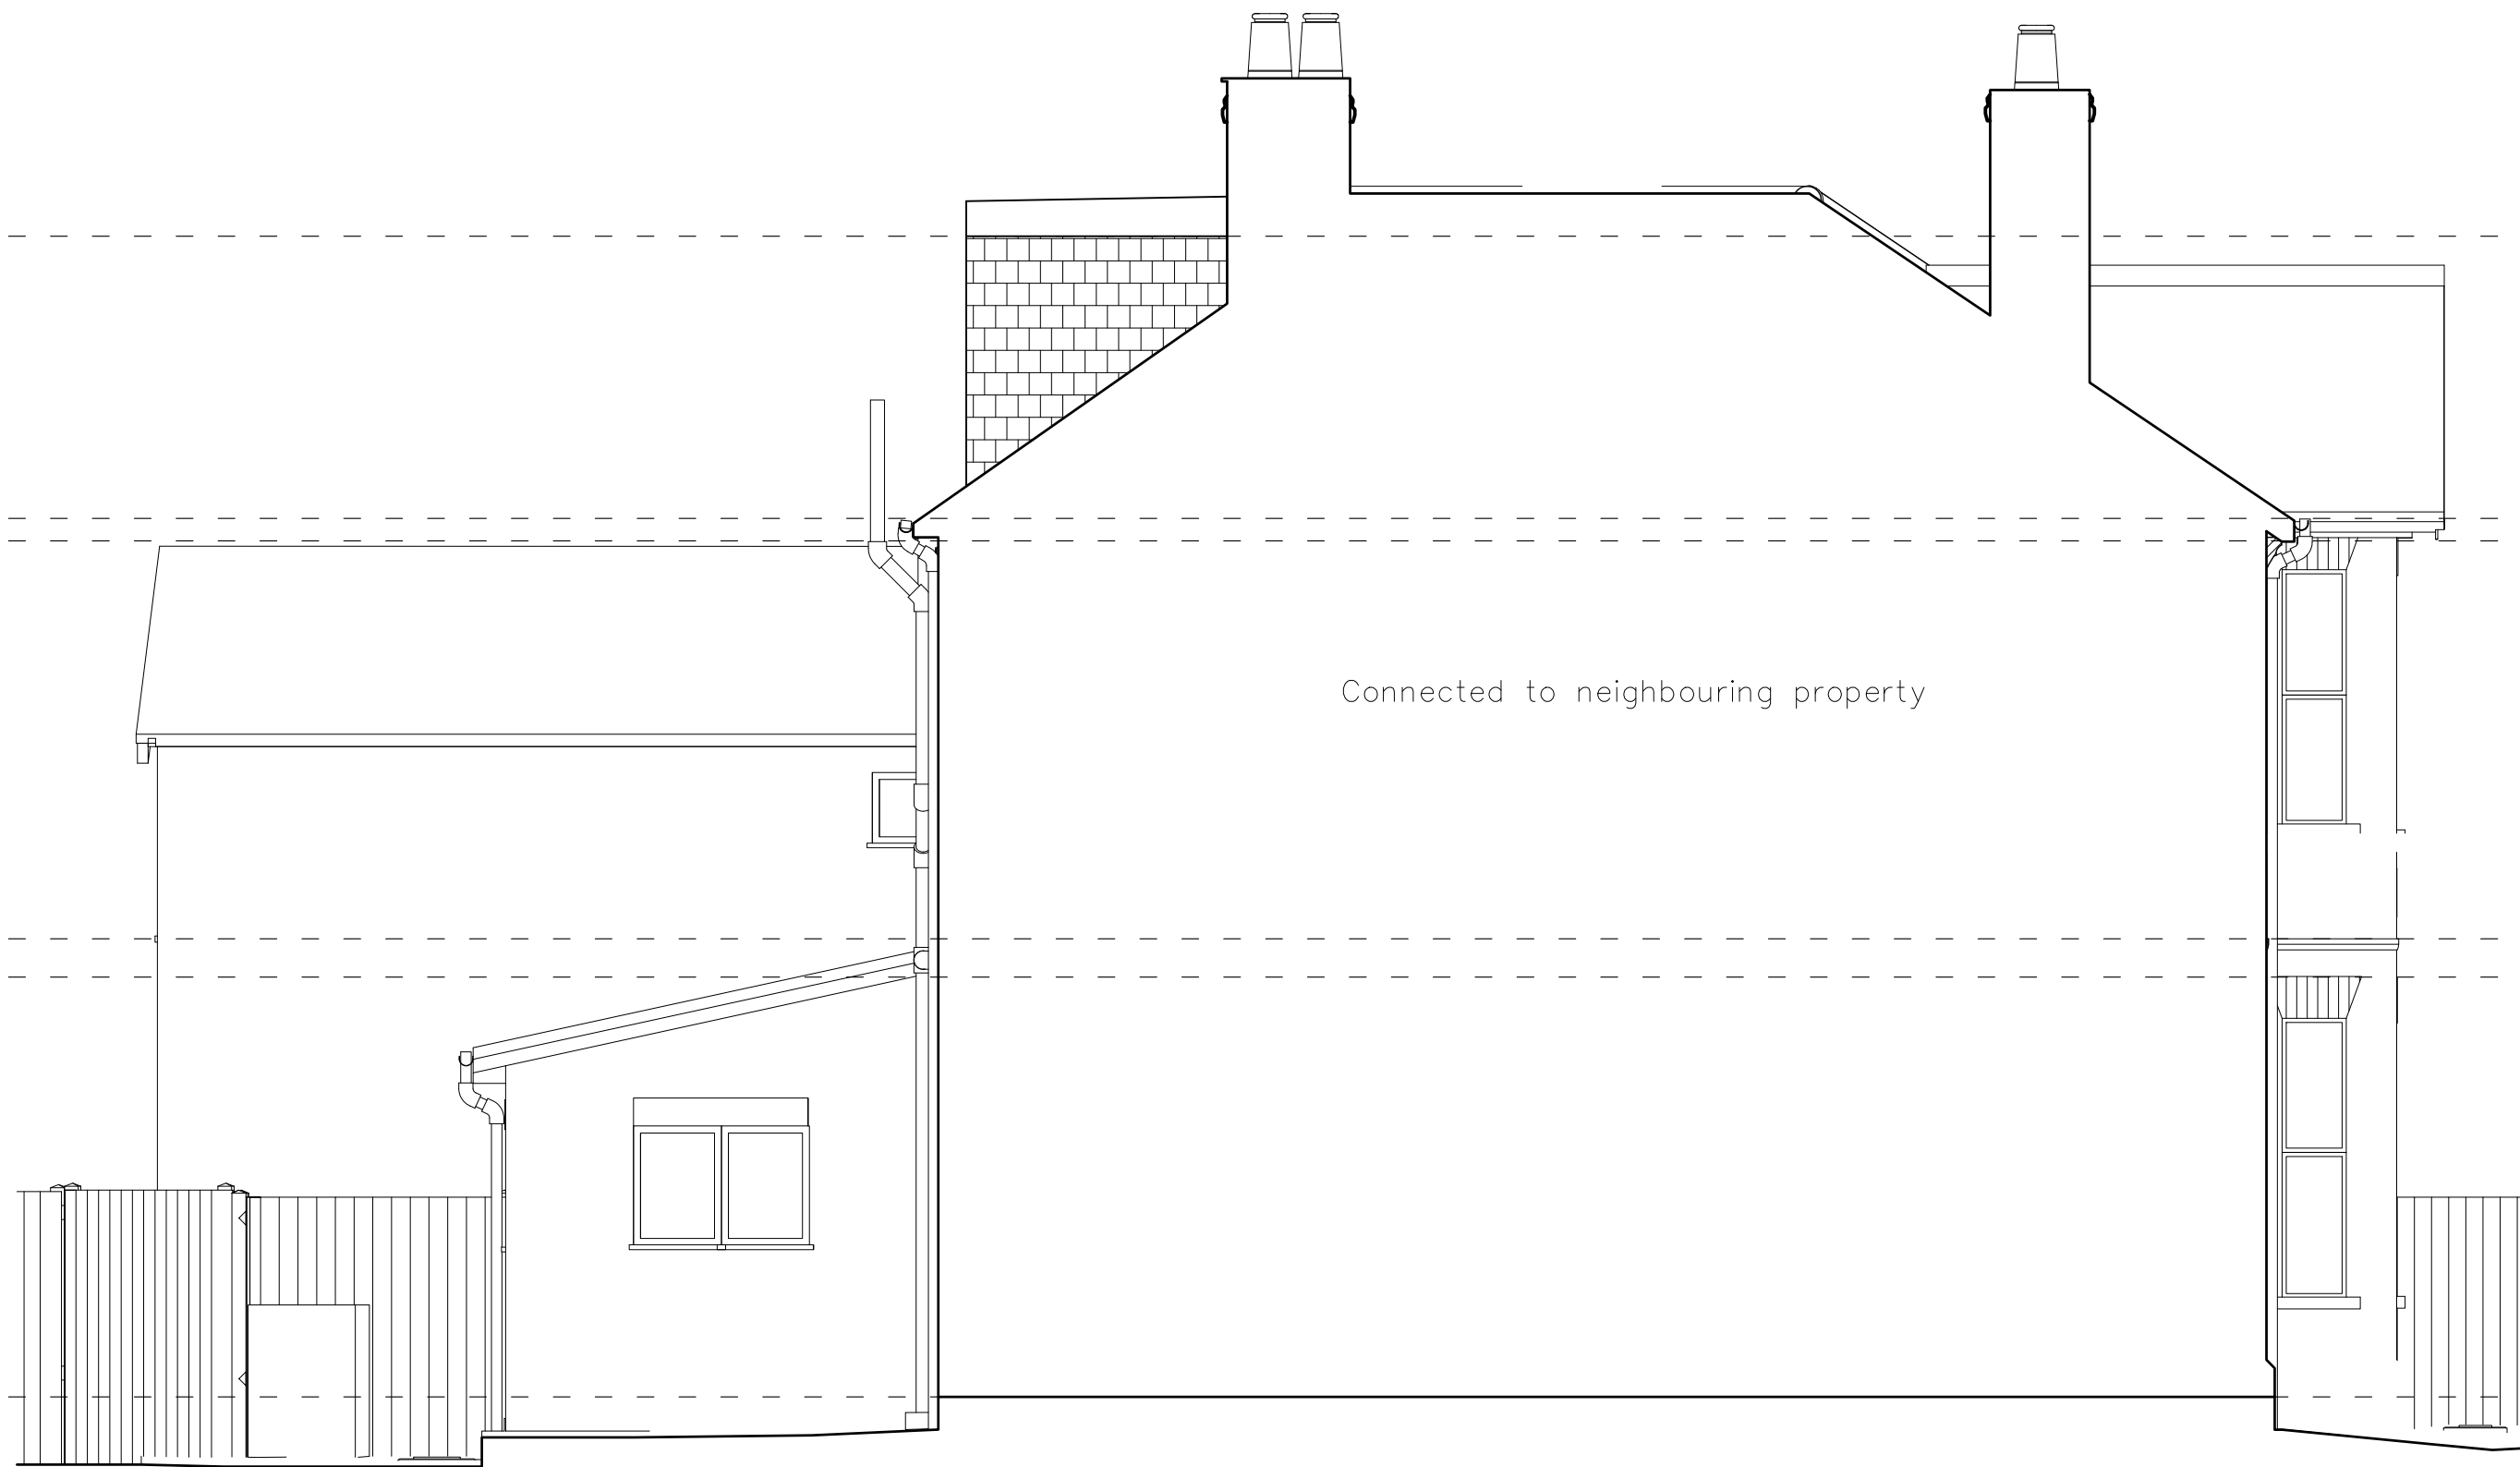

PROPOSED FLANK ELEVATION



PROPOSED REAR ELEVATION



PROPOSED FLANK ELEVATION

GENERAL NOTES

1. THE CONTRACTOR MUST CHECK ALL DIMENSIONS ON SITE BEFORE COMMENCING WORK
2. ANY DISCREPANCIES MUST BE IMMEDIATELY BROUGHT TO THE ATTENTION OF THE DESIGNER
3. ALL WORK MUST CONFORM TO CURRENT BUILDING REGULATIONS, BRITISH STANDARDS & CODES OF PRACTICE AND NHBC STANDARDS
4. THESE DRAWINGS ARE TO BE READ IN CONJUNCTION WITH ALL RELEVANT DESIGNER, ENGINEER OR SPECIALIST DRAWINGS AND SPECIFICATIONS
5. ALL DIMENSIONS ARE IN MILLIMETERS UNLESS STATED OTHERWISE
6. ALL MATERIALS ARE TO BE USED AND INSTALLED IN STRICT COMPLIANCE WITH THE RELEVANT MANUFACTURER'S RECOMMENDATIONS
7. THE CONTRACTOR IS RESPONSIBLE FOR PROVIDING ALL NECESSARY TEMPORARY SUPPORT TO THE BUILDING AND ANY ADJACENT STRUCTURES
8. ALL CONSTRUCTION MUST BE BUILT WITHIN THE ACTUAL PROPERTY BOUNDARIES UNLESS PARTY WALL AGREEMENT ALLOWS OTHERWISE


HATCH/LINE LEGEND (plans and sections)

	concrete		demolish
	brickwork		above/beyond
	blockwork		boundary
			drain
			insulation/ stud partition

DRAINAGE ABBREVIATIONS

mh	=	manhole
ic	=	inspection chamber
re	=	rodding eye
g	=	gully
svp	=	soil vent pipe
rwp	=	rain water pipe
ss	=	stub stack
		rainwater drainage to contractor design electrical layout to client design

REVISION	DESCRIPTION	DATE
----------	-------------	------

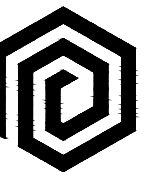

DRAW AND PLAN

T: 020 8243 8779

E: info@drawandplan.com

W: www.drawandplan.com

Location

**217 BOSTON ROAD
LONDON
W7 2AA**

Drawing title

GENERAL ARRANGEMENT

Date

24/03/2026

Scale

1:50@A1

Job no.

25100

Dwg no.

PGA003

Revision

-

